THE MIDLAND THEATRE

TECH PACK

Right in the heart of downtown Kansas City, this historic theatre has been entertaining the Midwest for almost 100 years. This gorgeous theatre has hosted world-famous talent and production, and a legendary venue with endless layouts to host and produce the perfect event for guests and fans.

PHYSICAL ADDRESS:
1228 MAIN STREET
KANSAS CITY, MO 64105

MAILING & SHIPPING ADDRESS:
8 W 13TH STREET
KANSAS CITY, MO 64105

Take a Tour: MidlandKC.com/virtual-tour

CONTACTS

Kim Baldwin	KBaldwin@AEGPresents.com	General Manager, The Midland
Lucas Bonewits	Lbonewits@AEGPresents.com	Production Manager, The Midland
Jeremy Bennet	jbennett@aegpresents.com	VIP/Merchandise
Grace Ekema	gekema@aegpresents.com	Box Office Manager

PARKING

- STREET PARKING ONLY. NO PRIVATE LOT AVAILABLE.
- THE PRODUCTION MANAGER WILL PROVIDE A SHOW SPECIFIC PARKING MAP ONCE ALL VEHICLES ARE ACCOUNTED FOR.
- SEMI TRUCKS AND BUSES WITH TRAILERS WILL PARK THE OPPOSITE DIRECTION OF TRAFFIC.
- SHORE POWER IS NOT AVAILABLE.

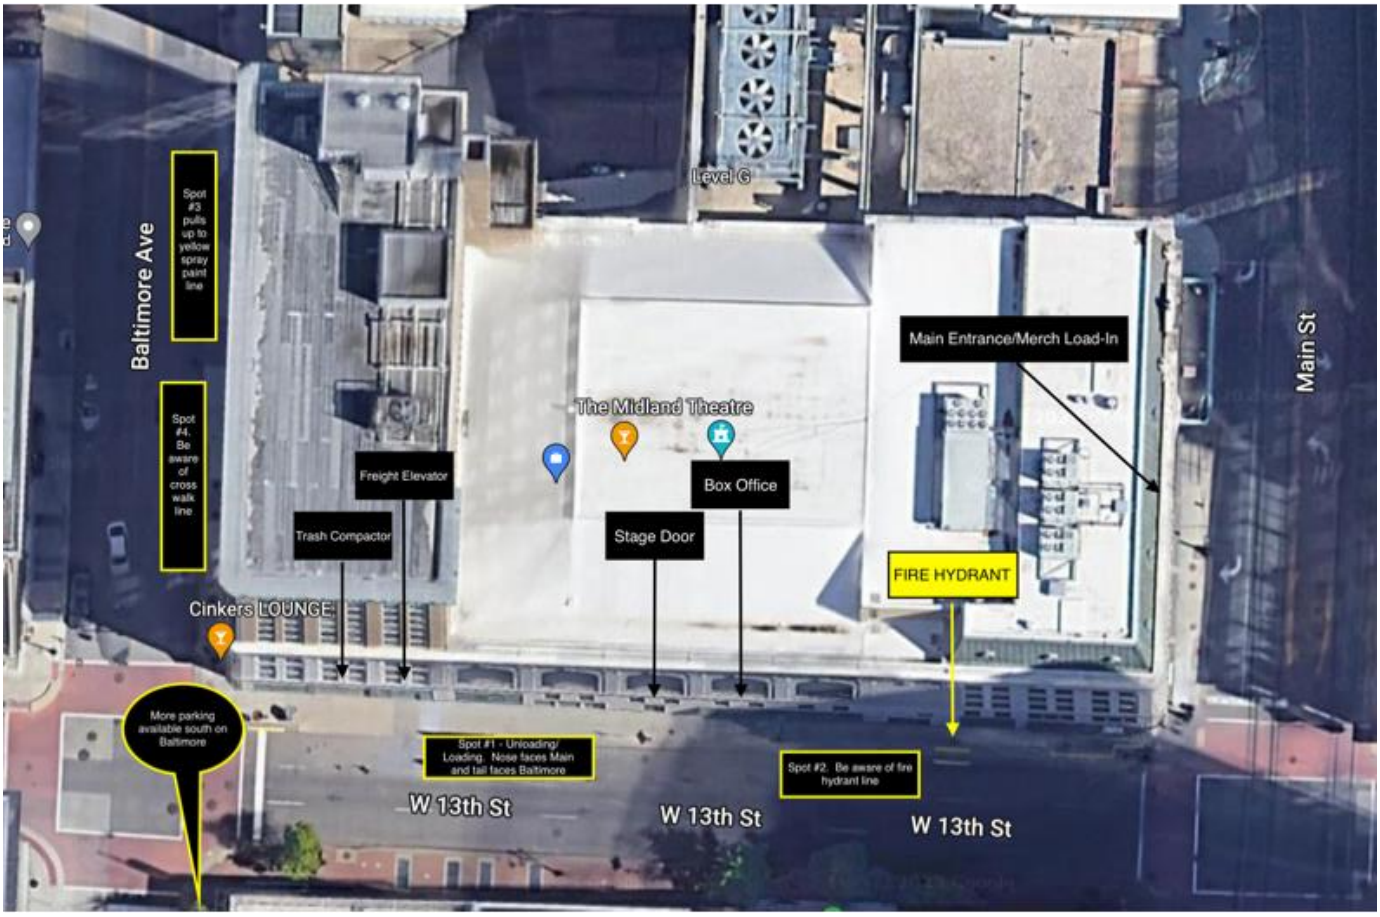

DRESSING ROOMS

ALL DRESSING ROOMS ARE LOCATED UPSTAGE AND ACCESSIBLE FROM LEFT OR RIGHT, IN CROSSOVER HALLWAY.

- THERE ARE 5 DRESSING ROOMS COMPLETE WITH RESTROOMS AND SHOWERS - 1 STAR, 2 LARGE, 2 SMALL.
- ALL DRESSING ROOMS ARE EQUIPPED WITH FURNISHINGS SUCH AS MIRROR, COUCH, TABLES, ETC.
- OUR CATERING ROOM IS FURNISHED AND INCLUDES 2 REFRIGERATORS

IN ADDITION TO THE ROOMS LISTED ABOVE, THERE ARE 2 PUBLIC RESTROOMS WITH SHOWERS.

WI-FI

WIFI IS AVAILABLE THROUGHOUT THE VENUE. LOGIN CREDENTIALS ARE POSTED IN ALL DRESSING ROOMS. HARD WIRED INTERNET IS AVAILABLE IN THE TOURING PRODUCTION OFFICE.

TECH

BACKSTAGE MAP

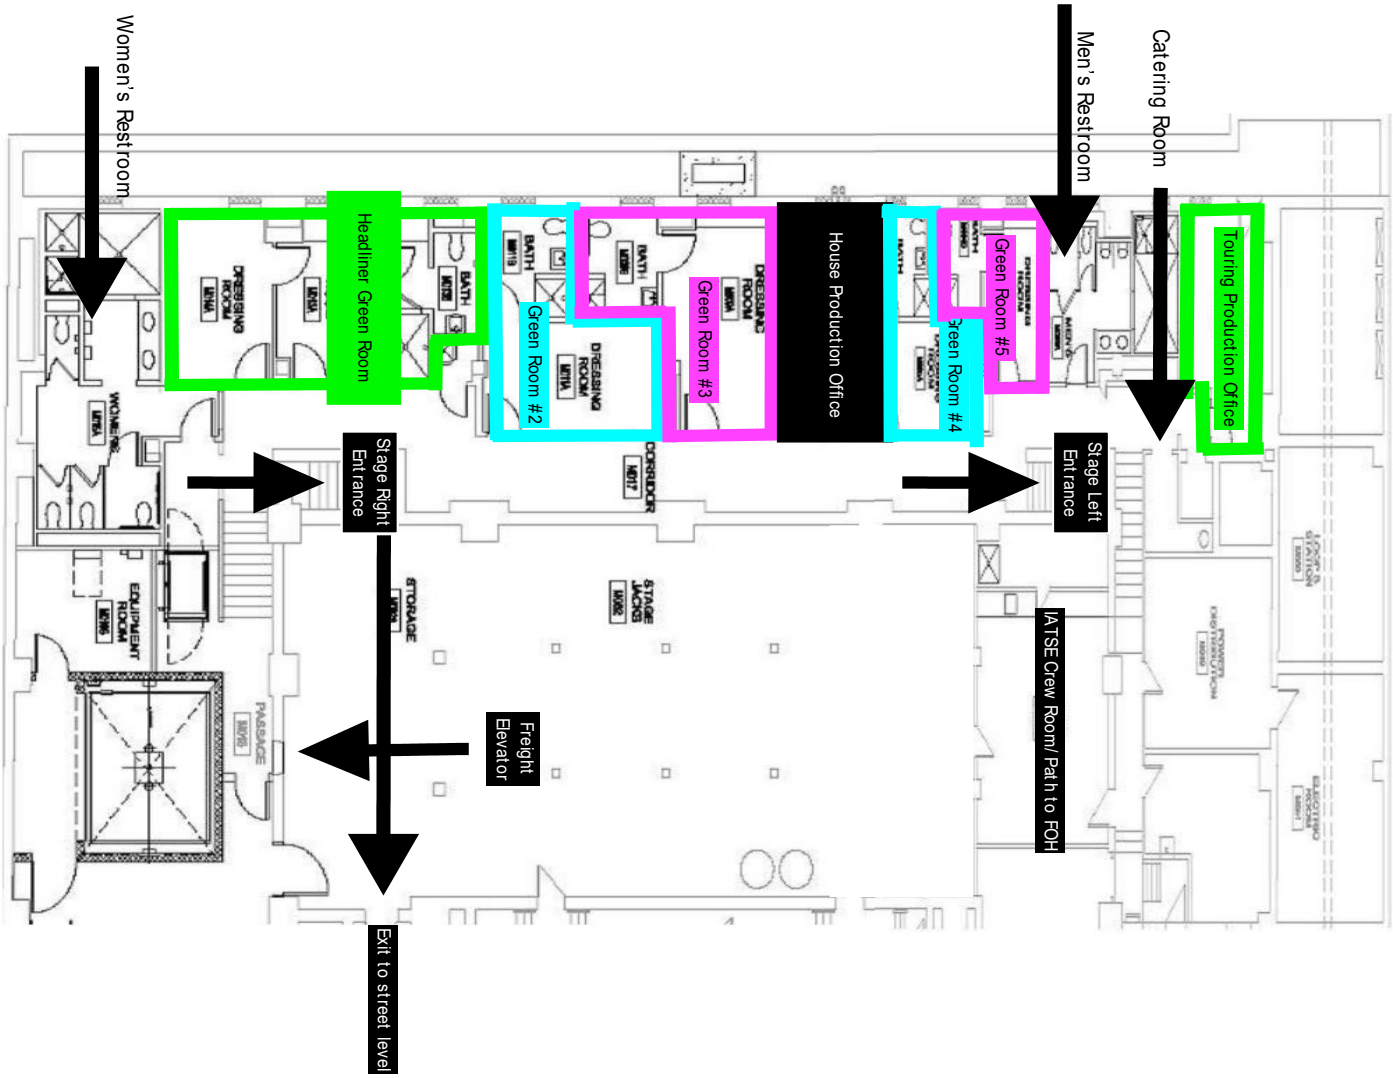

The Midland Stage and Backstage Layout

TOUR PRODUCTION OFFICE

THE TOURING PRODUCTION OFFICE IS LOCATED AT THE END OF THE DRESSING ROOM HALLWAY, JUST PAST THE SL ENTRANCE.

TECH

LAUNDRY

OUR VENUE IS EQUIPPED WITH BOTH A WASHER AND DRYER. THEY ARE LOCATED IN THE SL STORAGE ROOM, BEHIND THE FREIGHT ELEVATOR.

MERCHANDISE

THE MERCHANDISE AREA IS LOCATED IN OUR FRONT LOBBY. WE CAN ACCOMMODATE UP TO 13FT OF SPACE VIA OUR PERMANENT MERCH COUNTER.

PLEASE CONTACT OUR OPERATIONS COORDINATOR, ANDREA SEPUT WITH ANY QUESTIONS OR TO ADVANCE: ASEPUT@AEGPRESENTS.COM

SECURITY

IF YOU WISH TO SEE THE MIDLAND THEATRE EMERGENCY RESPONSE PLAN, PLEASE REACH OUT TO OUR GENERAL MANAGER, KIM BALDWIN AT KBALDWIN@AEGPRESENTS.COM.

WE DO NOT PUBLISH OUR ERP TO A PUBLIC SITE. WE HOPE YOU UNDERSTAND.

ALL PATRONS WILL PASS THROUGH OUR OPEN GATE SYSTEM AT ENTRY. STAGE DOOR MAY BE EQUIPPED WITH A METAL DETECTOR UPON REQUEST.

LOAD IN AND STORAGE

FROM SPOT #1, IT IS A SHORT PUSH ON A PUBLIC SIDEWALK TO A FREIGHT ELEVATOR (11’ 4” WIDE X 7’ 11” TALL X 10’ 1” DEEP) DOWN ONE LEVEL, DIRECTLY TO THE STAGE. THIS IS THE ELEVATOR AT STREET LEVEL.

FROM ELEVATOR TO STAGE. JUST UNDER 8’ WIDE X 7’ 11” HIGH

THE PRIMARY DEAD CASE STORAGE IS LOCATED DIRECTLY RIGHT OF THE ELEVATOR BEFORE THE DOUBLE DOORS LEADING TO THE STAGE. THIS IS ALSO WHERE THE WASHER AND DRYER ARE LOCATED.

TECH

STAGING & POWER

STAGE & FOH

- ENTIRE DECK AREA + WINGS – 86’ WIDTH X 34’ DEPTH X 3’5” HEIGHT
- VIEWABLE PERFORMANCE AREA – 47 10” WIDTH X 28’ DEPTH X 3’5" HEIGHT
- TRIM (STAGE TO GRID) – 60’
- SNAKE RUN FROM SR OR SL – MINIMUM 180’
- DISTANCE FROM DOWNSTAGE EDGE TO FOH – 70’
- DISTANCE FROM UPSTAGE CURTAIN TO FOH – 103’
- FOH WIDTH – VARIABLE WITH BLOW THRU BARRICADE
- FOH DEPTH – 12’

ADDITIONAL DETAILS SENT UPON REQUEST

POWER

- ALL POWER IS LOCATED SL
- 400A LIGHTING POWER
- 200A AUDIO POWER
- IN-HOUSE SYSTEMS DRAW FROM THIS POWER

RISERS

- (12) 4X8 RISERS WITH 12” OR 24” HEIGHT
- ALL RISERS ARE STATIC OR ROLLING

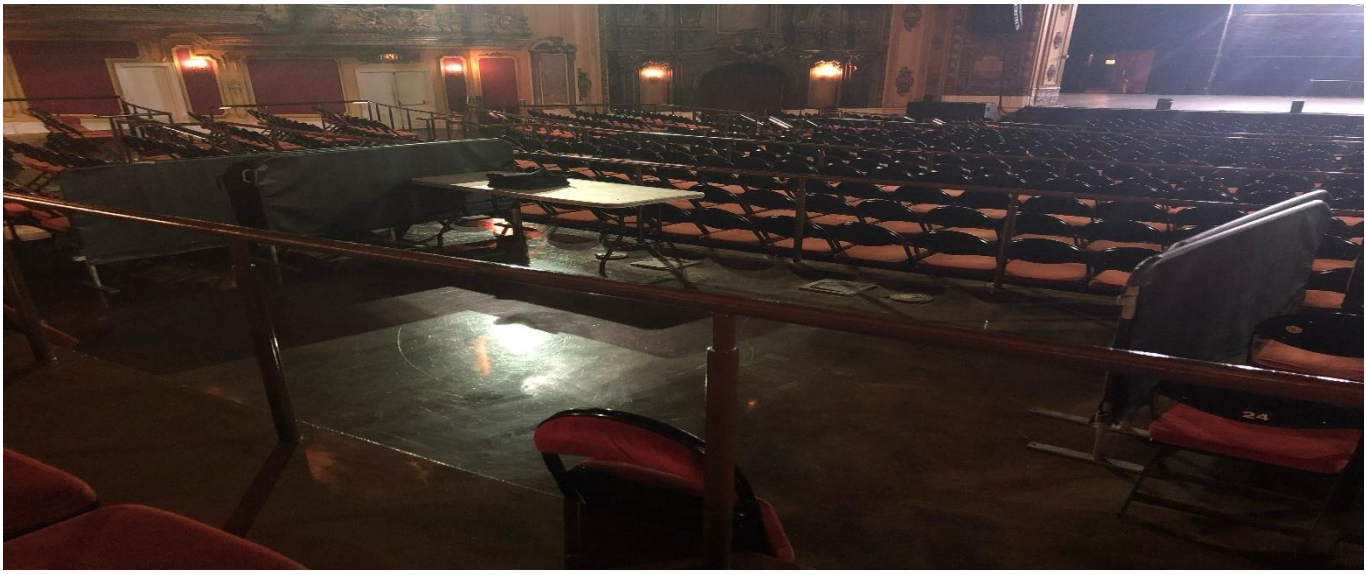

TECH

IN-HOUSE AUDIO

FOH SPEAKERS

L'ACOUSTICS K2 (24)	MAIN HANG - 12 PER SIDE
L'ACOUSTICS KARA II (8)	MAIN HANG - 4 PER SIDE
L'ACOUSTICS KS28 (12)	MAIN SUBS – 6 PER SIDE ON
L'ACOUSTICS A10I (6)	FLR UNDER BALCONY FILLS
L'ACOUSTICS X8 (4)	FRONT FILL

L'ACOUSTICS LA12X AMPLIFIER (17)-INCLUDES MONITORS
L'ACOUSTICS AVB P1 PROCESSOR (1)

MONITOR SPEAKERS

L'ACOUSTICS X15 HIQ (10)

L'ACOUSTICS X15 AND KS21 DRUM FILL (1)
L'ACOUSTICS KS21 SUBS/A15 SIDEFILLS (4)

CONSOLES

2 YAMAHA CS-R3 RIVAGE PM3 (FOH & MONITOR)

IN-HOUSE AUDIO

MICROPHONES & DI

6X SENNHEISER E604'S
5X SHURE SM58'S
8X SHURE BETA 58A'S
6X SHURE SM57'S
4X SHURE KSM137'S
1X BETA 91A
2X SHURE WL 184'S
1X SHURE PGA48 SWITCHED MIC'S
2X SHURE BETA 52'S
4X SENNHEISER E609'S
1X AT PRO 41 CARDIOID MIC
4X WHIRLWIND PCDI STEREO PASSIVE DIRECT BOX DI'S 9X COUNTRYMAN 85 DI'S
2X RADIAL PROD2 STEREO DI'S
2X RADIO J48 STEREO ACTIVE DI'S
2X WHIRLWIND DIRECTOR PASSIVE DI'S

COMMS

- ALL COMMS ARE WIRED
- ALL POSITIONS HAVE COMMS IN PLACE WITH HEADSETS
- AN ADDITIONAL 6 PACKS AND HEADSETS ARE AVAILABLE FOR EXTRA POSITIONS

WIRELESS

- 1 SHURE AD2 HANDHELD TRANSMITTER
- 4 SHURE AD2 HANDHELD TRANSMITTER
- 2 SHURE AD2 LAV BELT PACK TRANSMITTER

DECIBEL LIMITATIONS

DUE TO THE ANTIQUE NATURE OF OUR FACILITY, WE HAVE A **MAXIMUM DECIBEL LIMIT OF 105DB.**

THIS IS TO PROTECT OUR PATRONS FROM ANY DAMAGE TO PLASTER OR FAÇADE THAT CAN FALL DUE TO THE VIBRATIONS

TECH

IN-HOUSE LIGHTING

ATMOSPHERE

(1) ULTRATEC RADIANCE HAZER

ANY HAZE REQUIRES A FIRE GUARD FROM THE CITY

PROJECTION/VIDEO

- 1X EIKI LC – X800 3 LCD PROJECTOR/12K LUMENS
- 1X 37’ WIDE X 19’ 6” HIGH SCREEN, PERMANENTLY HUNG ON THE FOURTH ELECTRIC, WHICH IS 22’ 5” FROM THE DOWNSTAGE EDGE OF THE APRON

CONSOLE

grandMA3 LITE

LIGHTING FIXTURES

(12) MARTIN MAC VIPER PROFILE
(4) MARTIN MAC VIPER PERFORMANCE
(6) MARTIN MAC 700 PROFILE
(4) MARTIN MAC 700 WASH
(8) MARTIN MAC 101(6/BALC, 2/PROSC)
(6) COLORADO 1-QUAD ZOOM TOUR
(10) SOURCE 4 PAR 6-BARS
(2) 8-LIGHT MOLEFAY
(2 SUPER TROUPER 2K SPOTLIGHTS
(2) LYCIAN LTI 400 SPOTLIGHTS

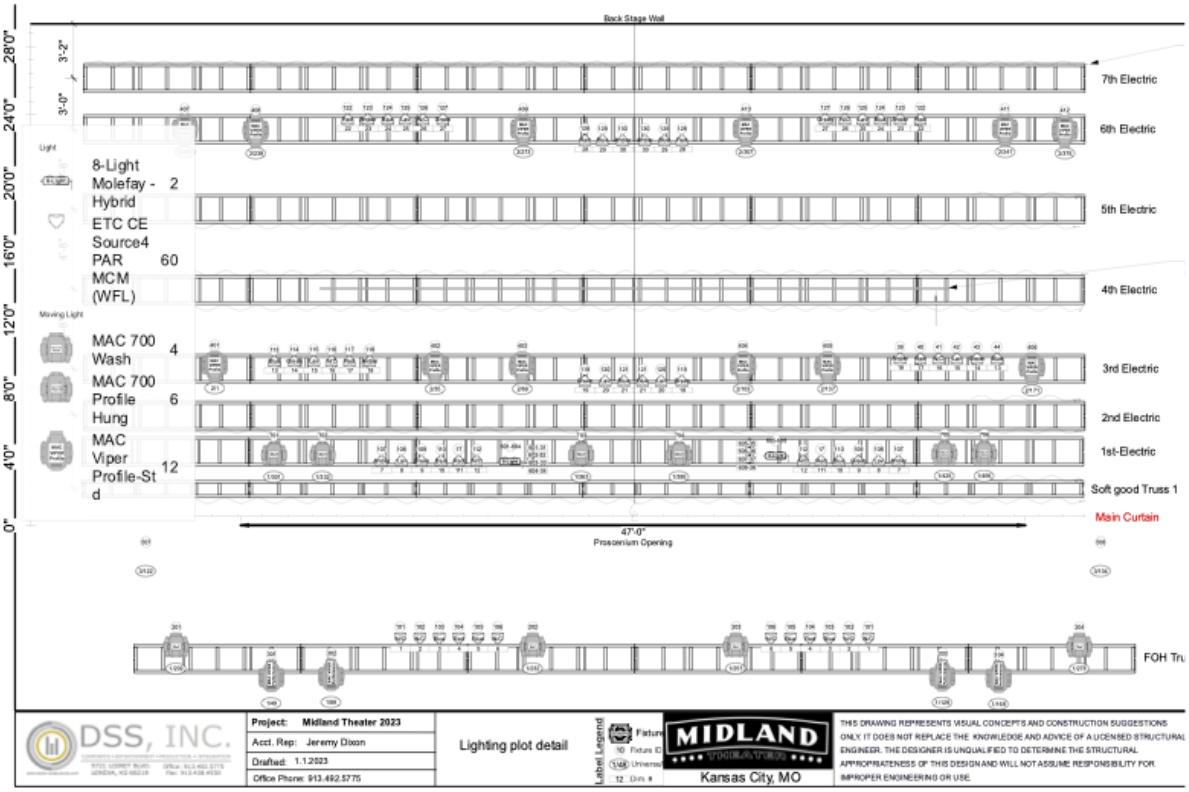

TECH

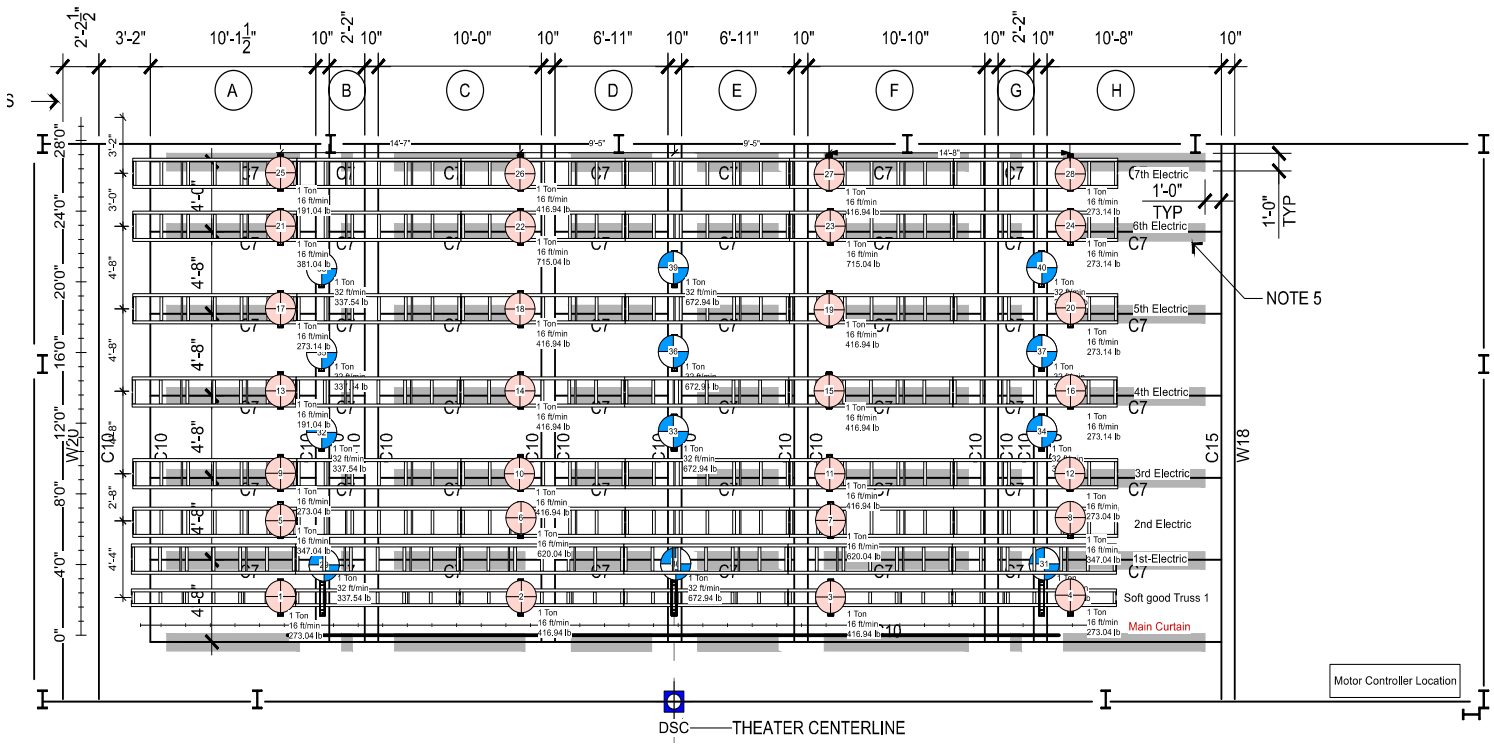

Hoist Symbols Used

Hoist 1 Ton Scenery Down

Hoist 1 Ton Super Grid Down

DSS, INC.
CORPORATE • ENTERTAINMENT • PRODUCTION • INTEGRATION
9721 LOIRET BLVD. LENEXA, KS 66219
Office: 913.492.5775 Fax: 913.438.4550

Project:	Midland Theater 2023
Acct. Rep:	Jeremy Dixon
Drafted:	1.1.2023
Office Phone:	913.492.5775

1 House Grid Plot
Scale: 1:68

MIDLAND THEATER
Kansas City, MO

THIS DRAWING REPRESENTS VISUAL CONCEPTS AND CONSTRUCTION SUGGESTIONS ONLY. IT DOES NOT REPLACE THE KNOWLEDGE AND ADVICE OF A LICENSED STRUCTURAL ENGINEER. THE DESIGNER IS UNQUALIFIED TO DETERMINE THE STRUCTURAL APPROPRIATENESS OF THIS DESIGN AND WILL NOT ASSUME RESPONSIBILITY FOR IMPROPER ENGINEERING OR USE.

MERCHANDISE

PLEASE ADVANCE WITH JEREMY BENNETT
JBENNETT@AEGPRESENTS.COM

- THE SHIPPING ADDRESS FOR ALL MERCH IS TO OUR BOX OFFICE: **8 WEST 13TH STREET, KANSAS CITY, MO 64105**
- PLEASE INCLUDE THE ARTISTS' NAME ON ALL PACKAGES BEING SHIPPED. **THE BOX OFFICE IS AVAILABLE FOR PICKUPS MONDAY TO FRIDAY, FROM 10:00 AM TO 5:00 PM, WITH VARYING HOURS ON SHOW DAYS.**
- WE DO NOT HAVE MERCHANDISE SPECIFIC CREDIT CARD MACHINES OR ATVENU AT THE MIDLAND
- TAX IS 11.975% AND TOURING PARTIES RETAIN
- IF YOU NEED BOXES/PACKAGES/ETC. SHIPPED OUT POST-SHOW, PLEASE EMAIL ANDREA WITH THE SHIPPING LABEL(S). WE WILL PLACE THEM IN THE BOX OFFICE FOR PICKUP. IT IS THE RESPONSIBILITY OF THE PERSON REQUESTING THE SHIPMENT TO SCHEDULE A PICKUP WITH THE SHIPPING COMPANY.

PLEASE NOTE: WE ARE NOT RESPONSIBLE FOR ANY ITEMS LEFT AT THE BOX OFFICE

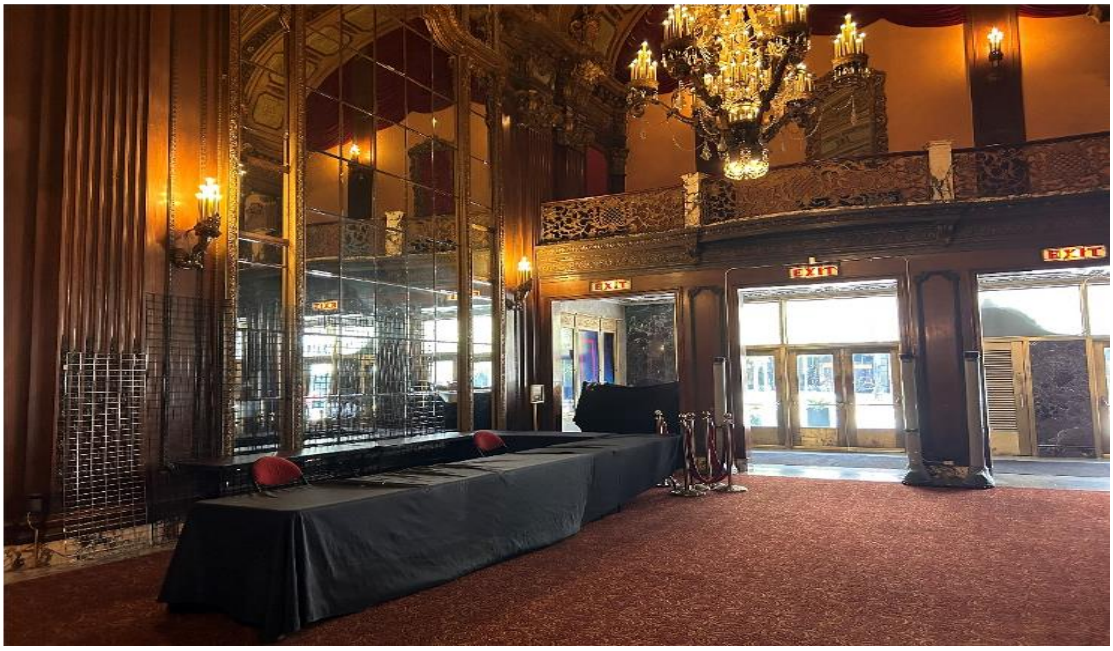

THE PRIMARY MERCHANDISE AREA IS LOCATED IN THE MAIN THEATRE LOBBY, DIRECTLY NEXT TO THE MAIN ENTRANCE. A SECONDARY LOCATION IS ALSO IN THE MAIN LOBBY, NEAR THE SOUTH ENTRANCE. WE HAVE SEVERAL RACKS AND TABLES AVAILABLE IN-HOUSE.

VIP INFORMATION

FOR ADVANCE & ANY QUESTIONS, PLEASE CONTACT JEREMY BENNETT:
JBENNETT@AEGPRESENTS.COM

TO ENSURE WE STAFF APPROPRIATELY AND PREPARE THE VENUE, PLEASE PROVIDE THE FOLLOWING INFORMATION:

- WHAT TIME WILL ACCESS TO CHECK-IN BEGIN?
- WHAT TIME DOES THE MEET & GREET START?
- WILL YOU PROVIDE GUEST CREDENTIALS?
- ARE GUESTS ALLOWED TO STAY IN THE BUILDING POST-MEET & GREET?
- WILL A SEPARATE ENTRANCE FOR CHECK-IN OR CREDENTIAL DISTRIBUTION BE REQUIRED? (ADDITIONAL STAFF MAY INCUR A FEE)
- PLEASE PROVIDE ALL DETAILS OF THE MEET AND GREET EXPERIENCE (E.G., STEP AND REPEAT, AUTOGRAPHS, ONE-ON-ONE TIME, PHOTOS)
- IF PHOTOS ARE INCLUDED, WILL THEY BE TAKEN WITH GUESTS' PHONES OR BY A PROFESSIONAL PHOTOGRAPHER WHO WILL PROVIDE A LINK WITHIN 48 HOURS?
- PLEASE PROVIDE ANY SPECIFIC SECURITY INSTRUCTIONS FOR OUR GUARDS

MIDLAND VIP PROGRAM CHARGES

INCLUDES TABLES, CHAIRS, LINES, PIPE AND DRAPE, SETUP ASSISTANCE, AND SECURITY

- **1-75 GUESTS: $250**
- **76-150 GUESTS: $400**
- **151-300 GUESTS: $500**

ADDITIONAL CHARGES MAY APPLY FOR:

- EXTRA SECURITY (E.G., UNIFORMED OFFICERS, ADDITIONAL GUARDS OR SUPERVISORS)
- MEET & GREET EXPERIENCES OVER TWO HOURS
- EVENTS WITH MORE THAN 300 GUESTS